



Grundriss Kellergeschoss:

(nicht maßstabsgetreu)

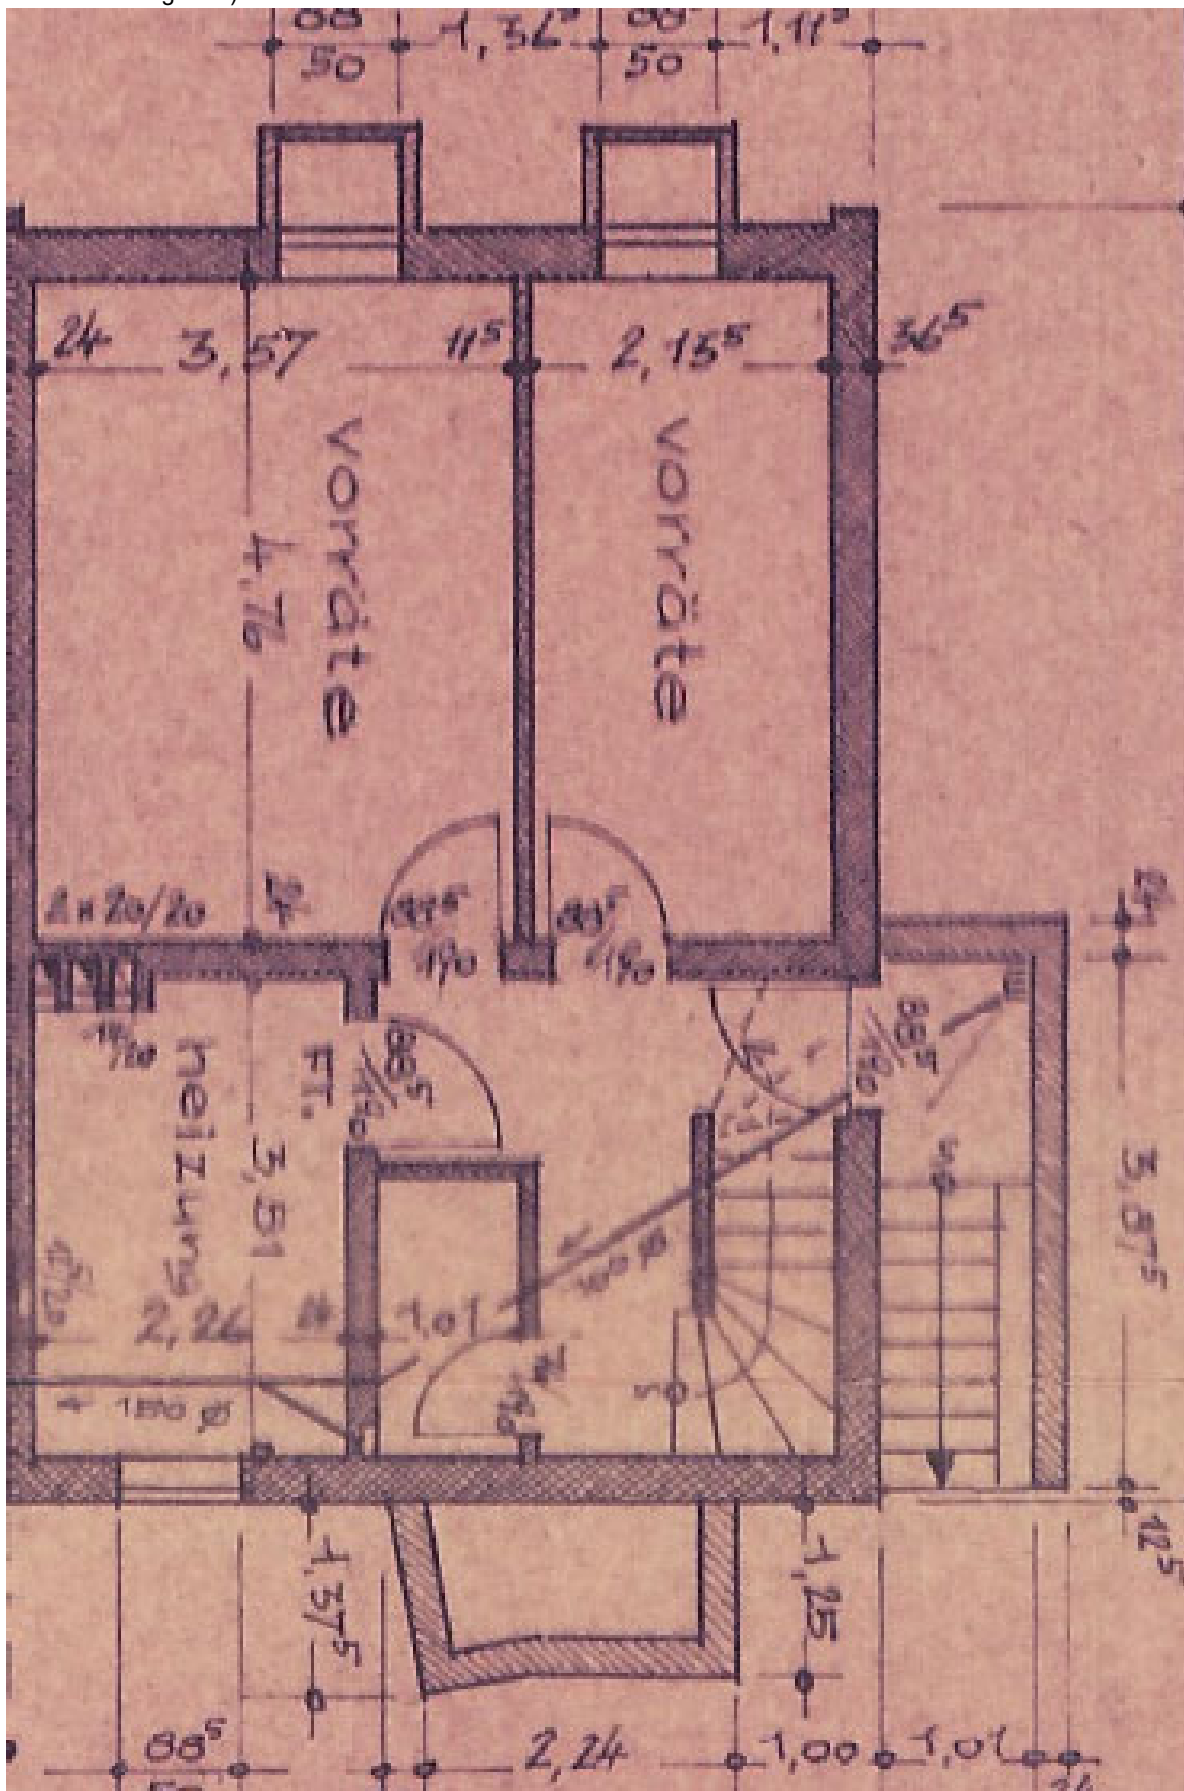


Grundriss Erdgeschoss:

(nicht maßstabsgetreu)

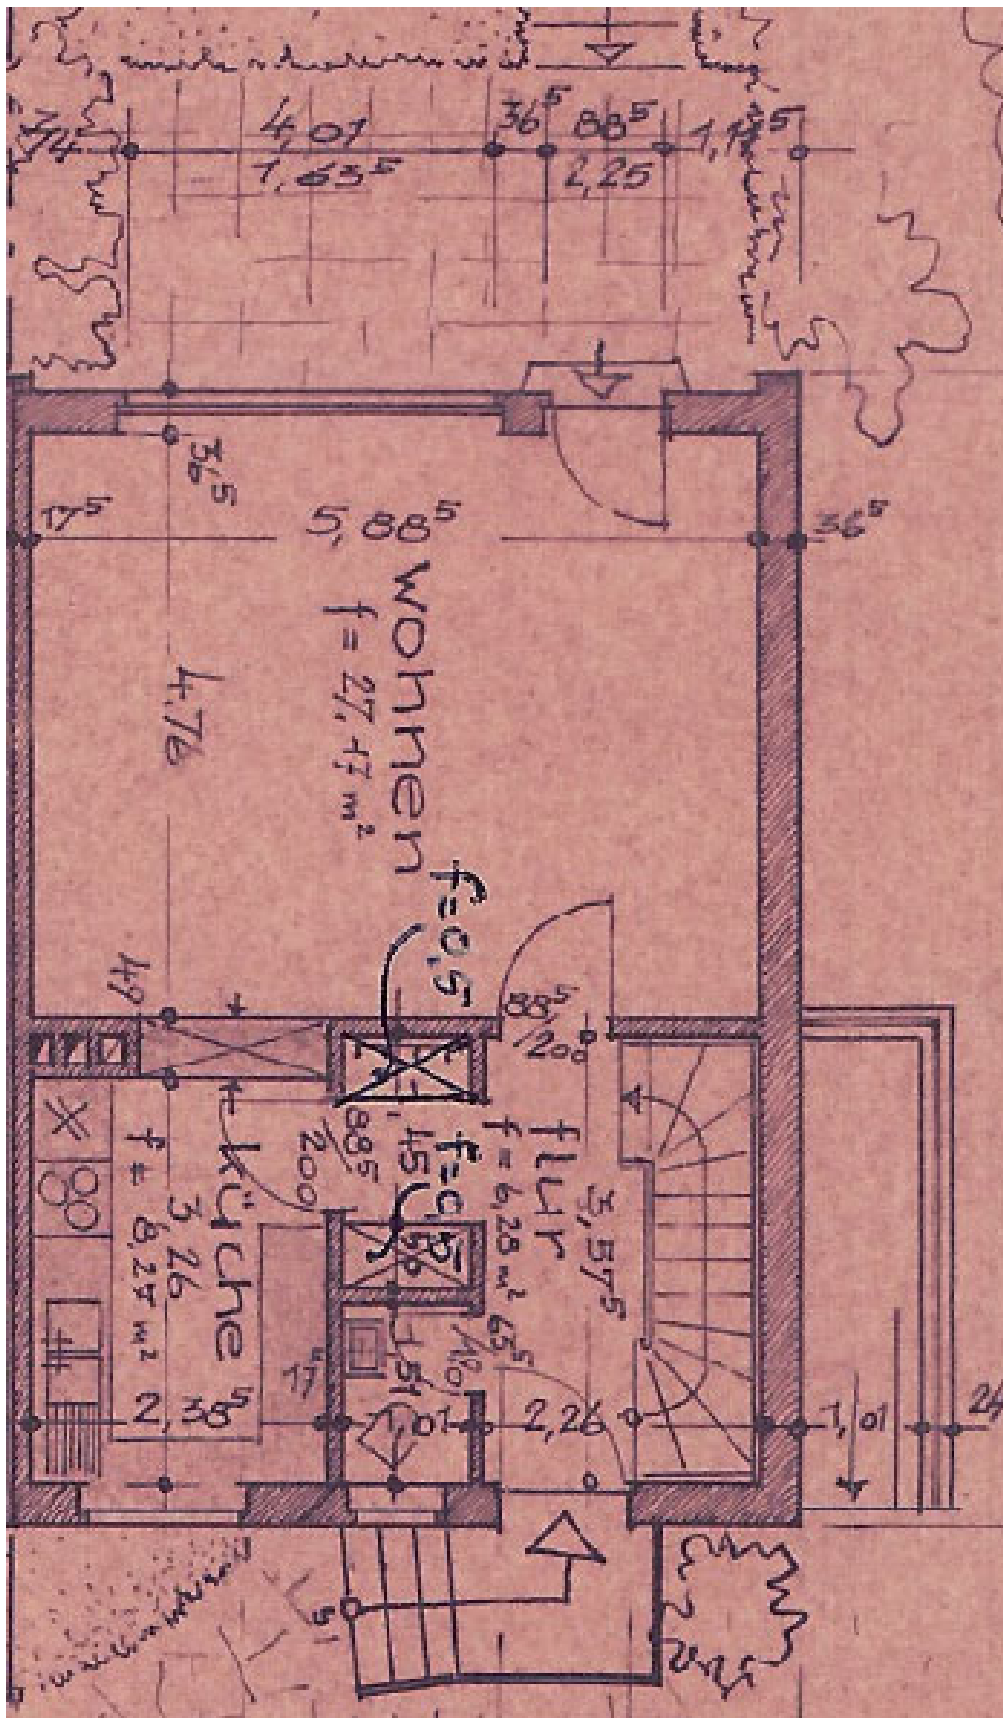


Grundriss Obergeschoss:

(nicht maßstabsgetreu)

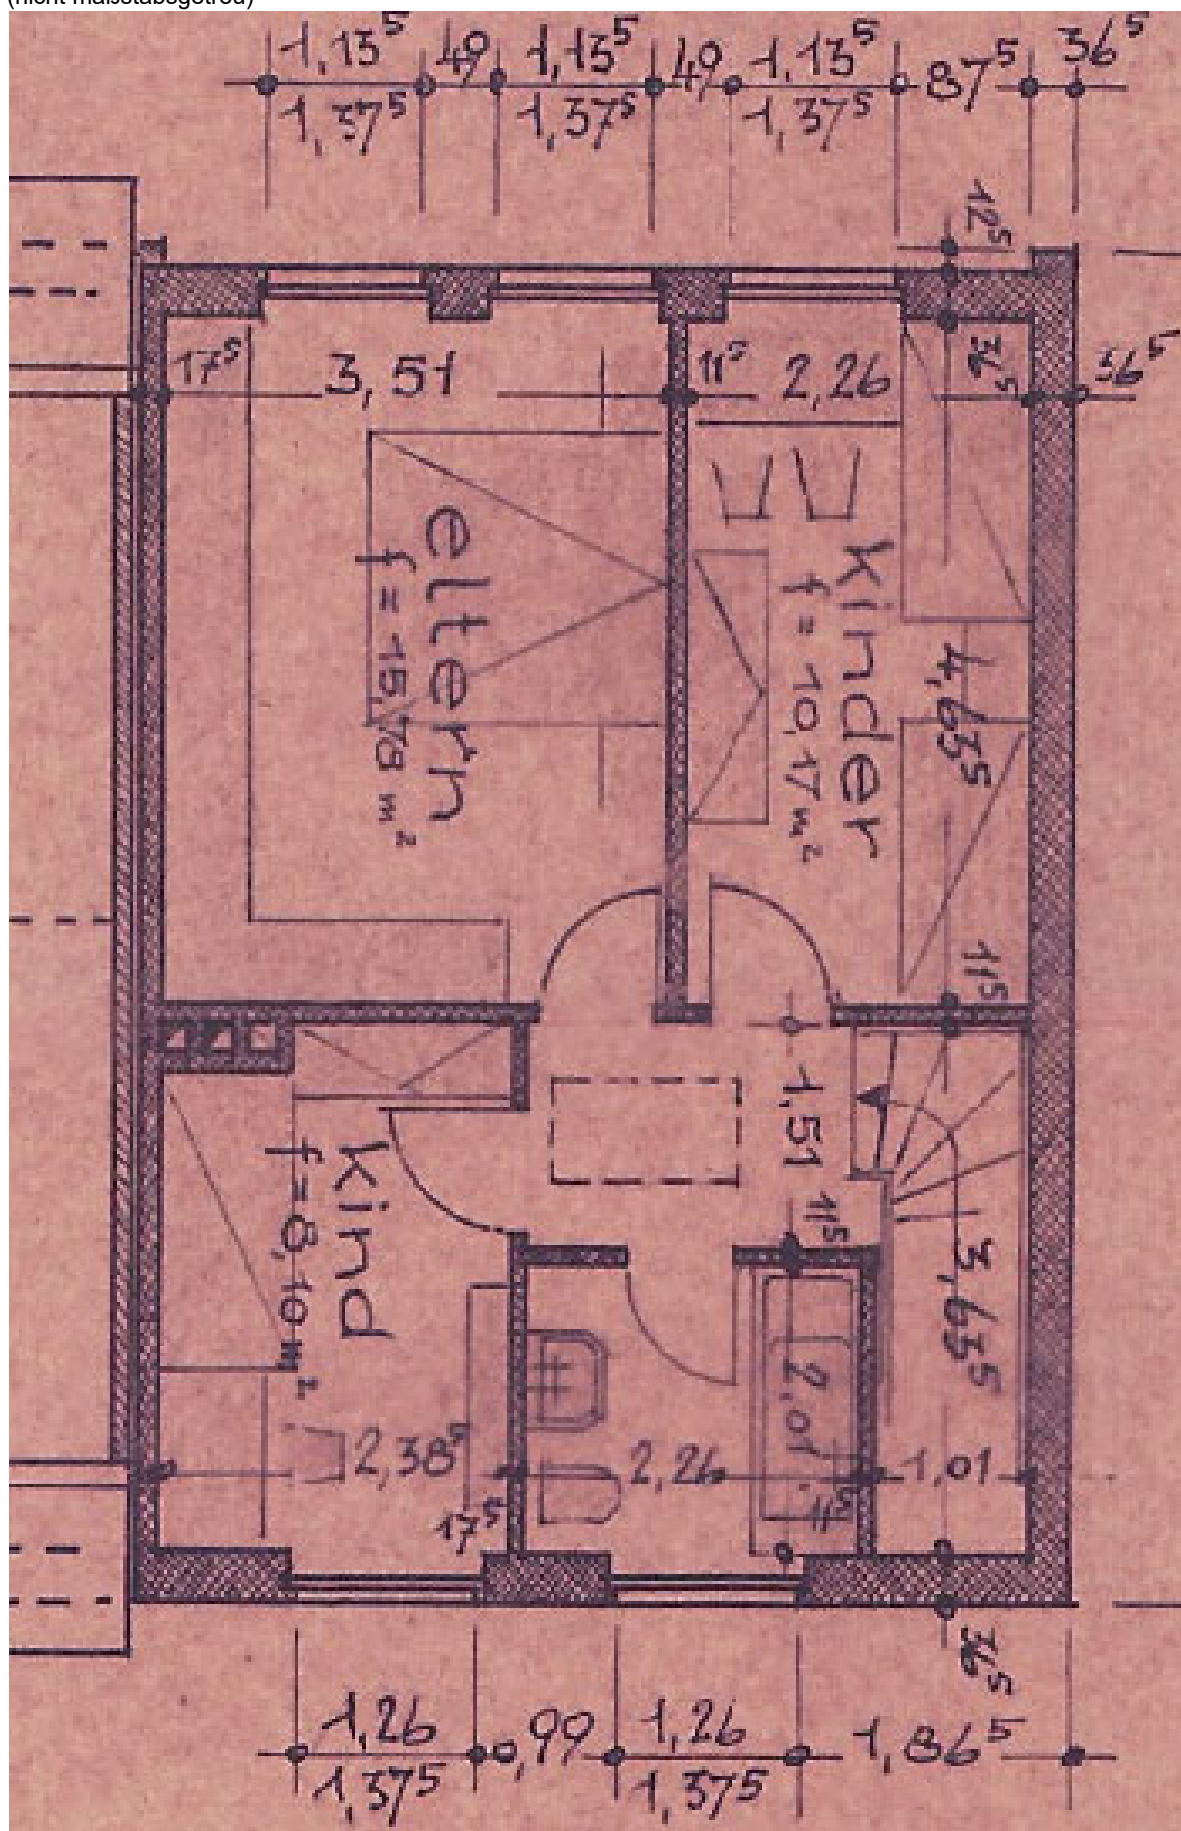


Schnitt:

(nicht maßstabsgetreu und Schnitt durch Nebengebäude, Höhen identisch)

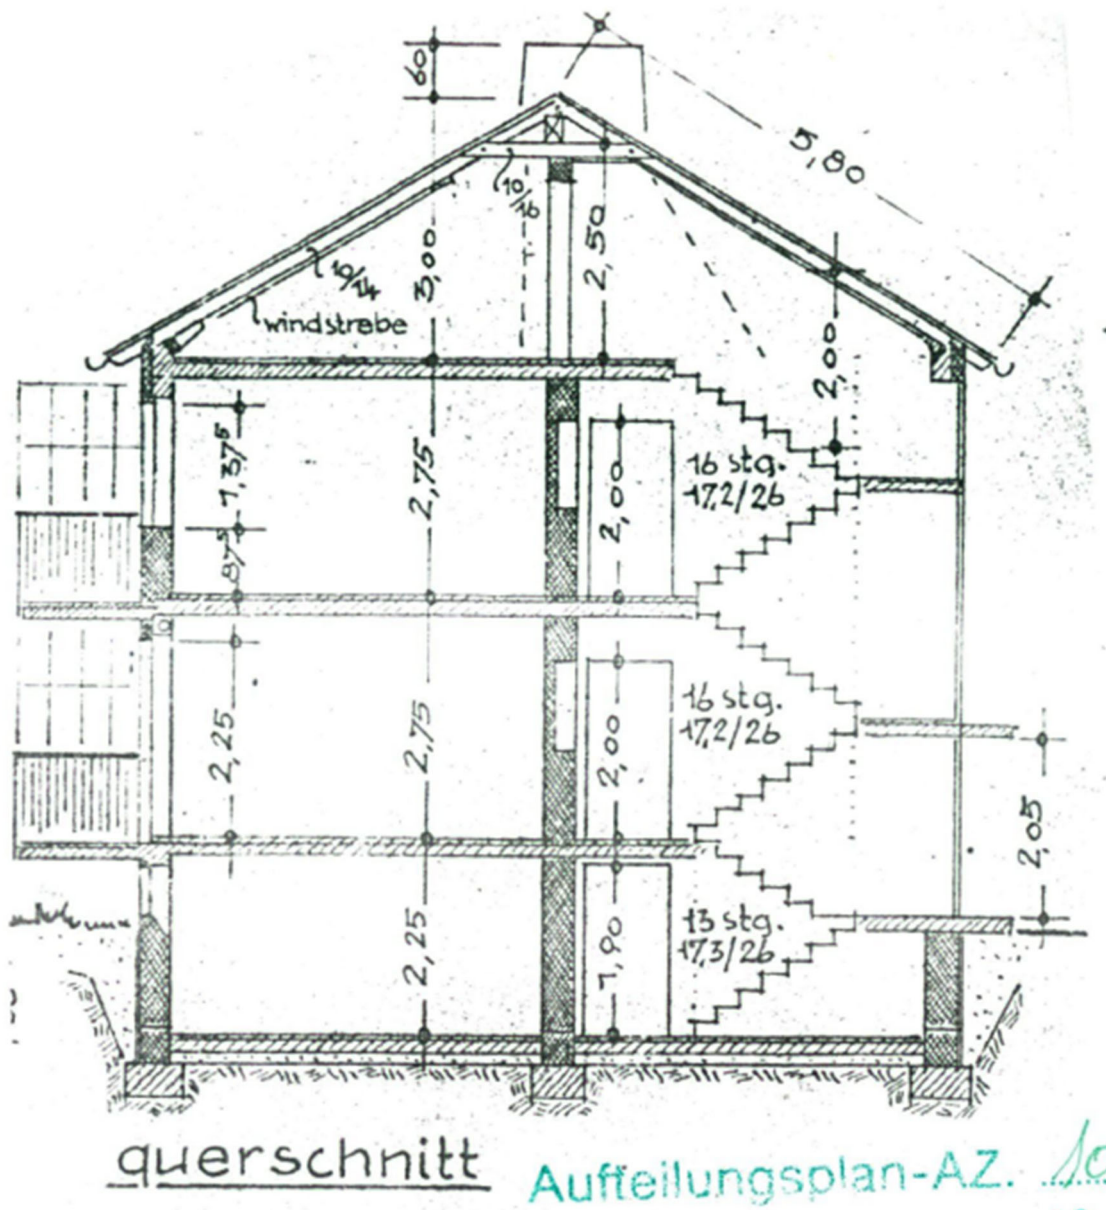

Grundriss Garage:

(nicht maßstabsgetreu)

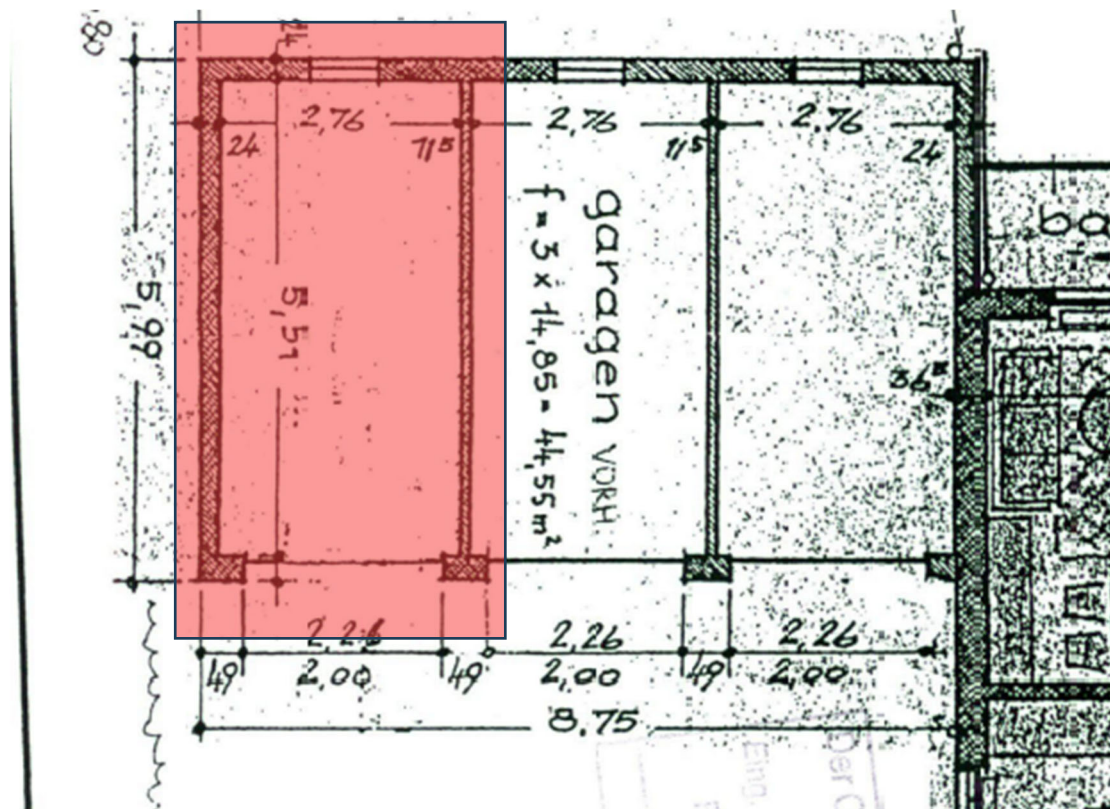

Schnitt Garage:

(nicht maßstabsgetreu)

